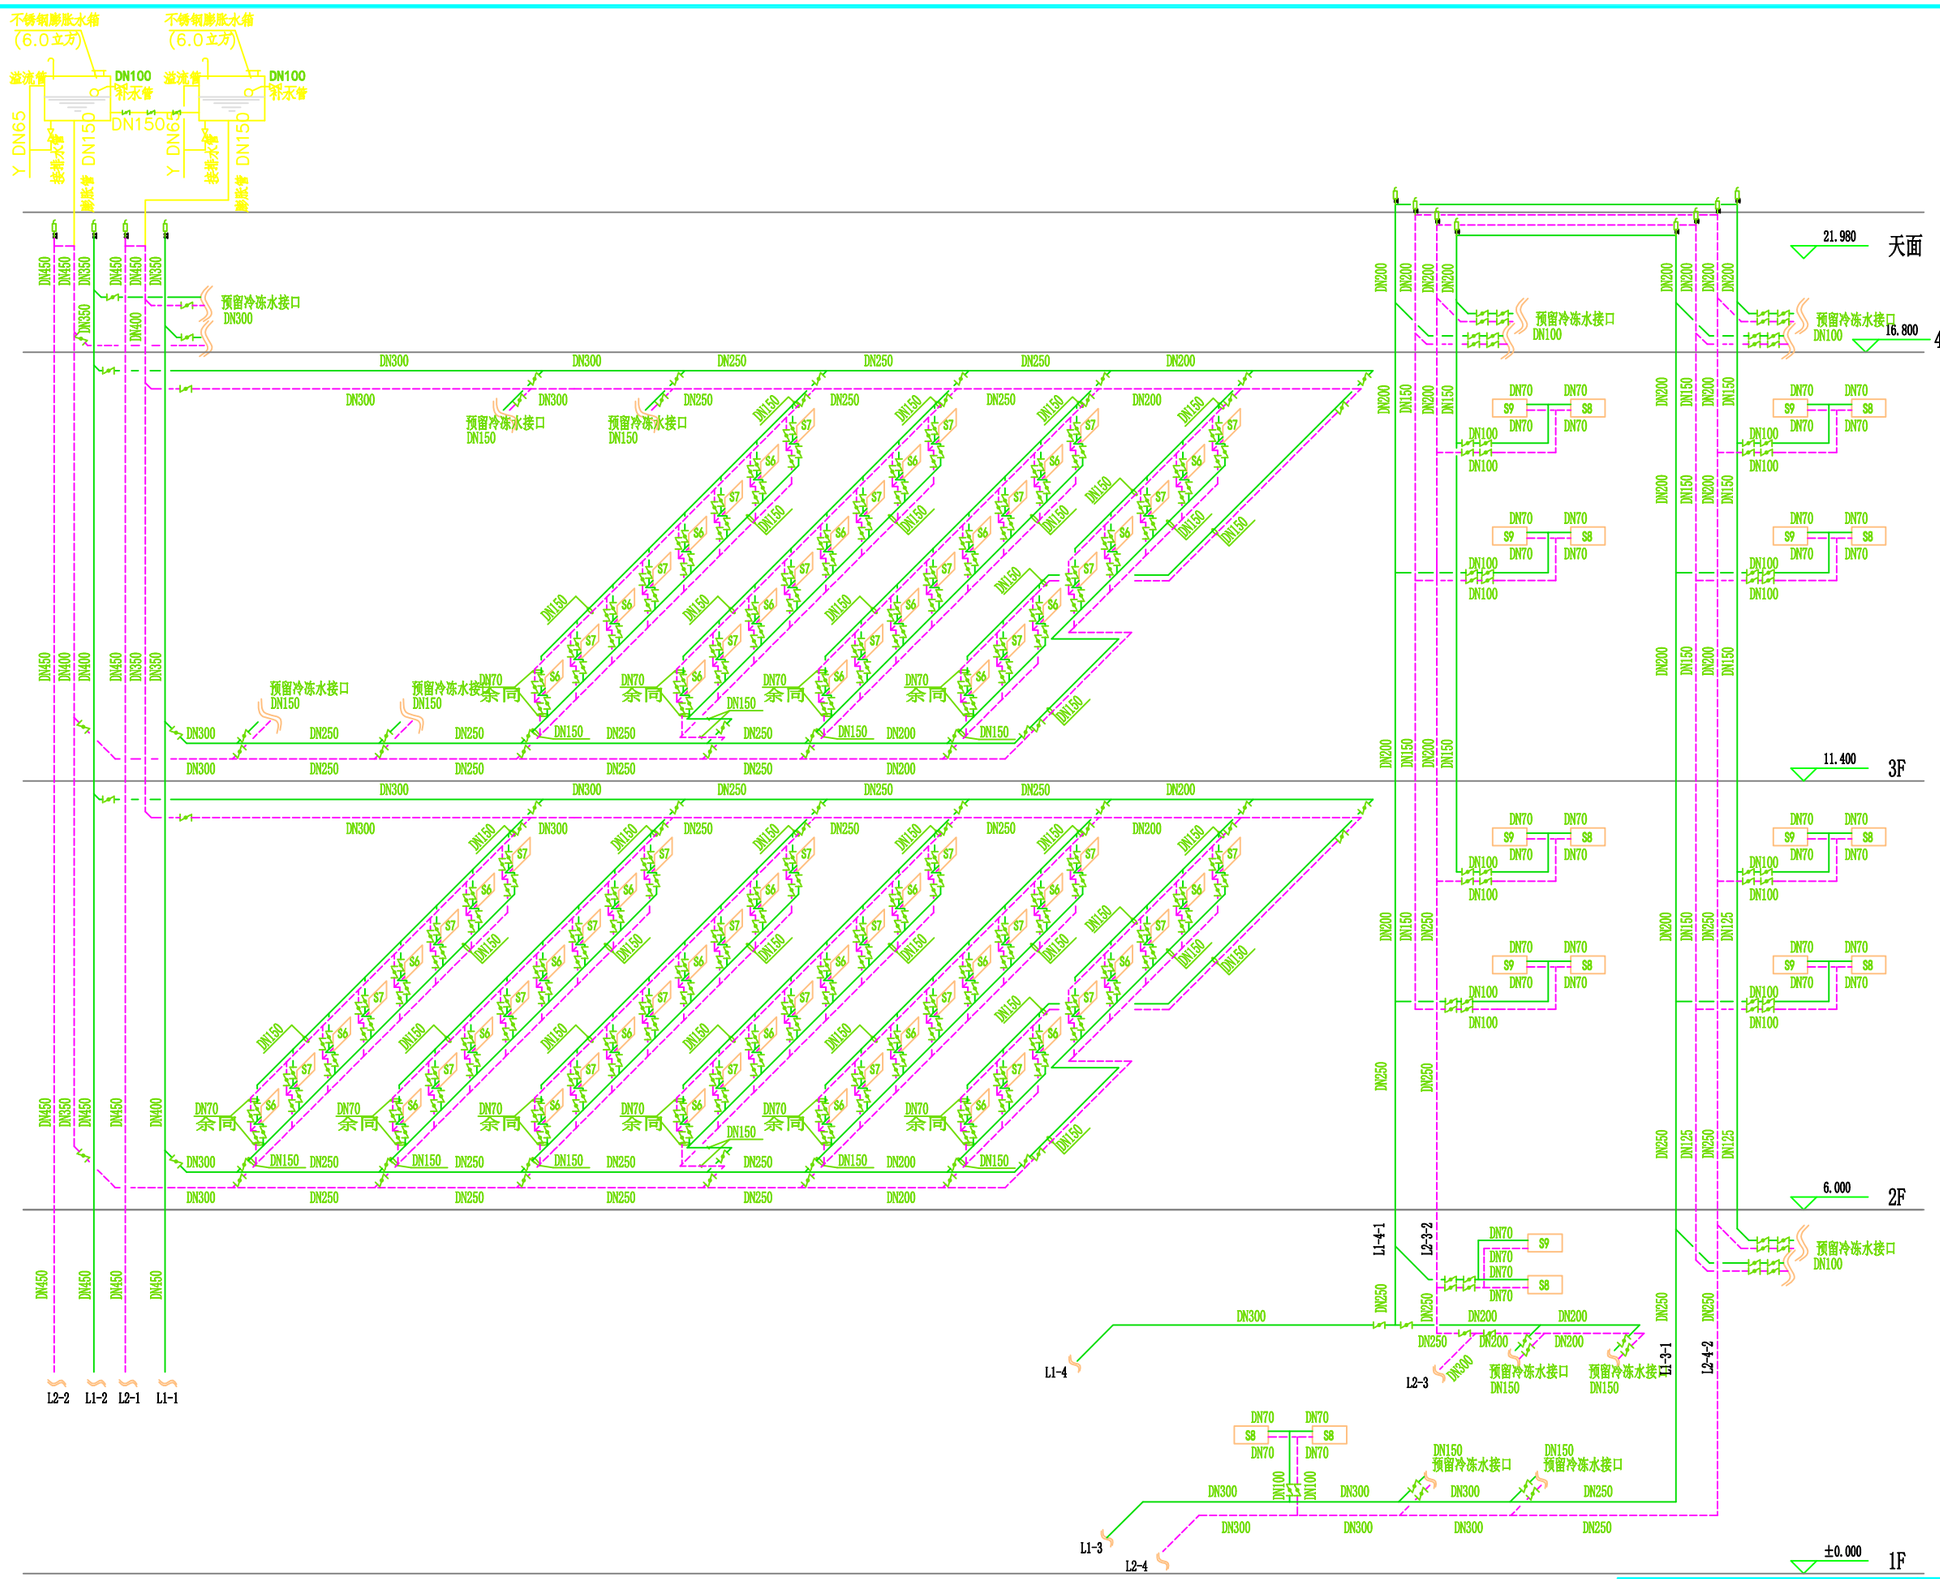

广东省电信规划设计院有限公司						工程名称	华润集团新一代数据中心建设工程（一期）1#数据中心楼
工程设计证书编号：（甲级）A144011751						建设单位	润联软件系统（深圳）有限公司
审 定	邓重秋		项目负责人	李卡卡		内 容	冷冻水立管系统图
审 核	许新毅		专业负责人	许新毅		设计编号	135728-01-0026
校 对	李双磊		设 计	熊玮恺		设计阶段	空 施
						图 号	FK-08
						日 期	2014.06.13