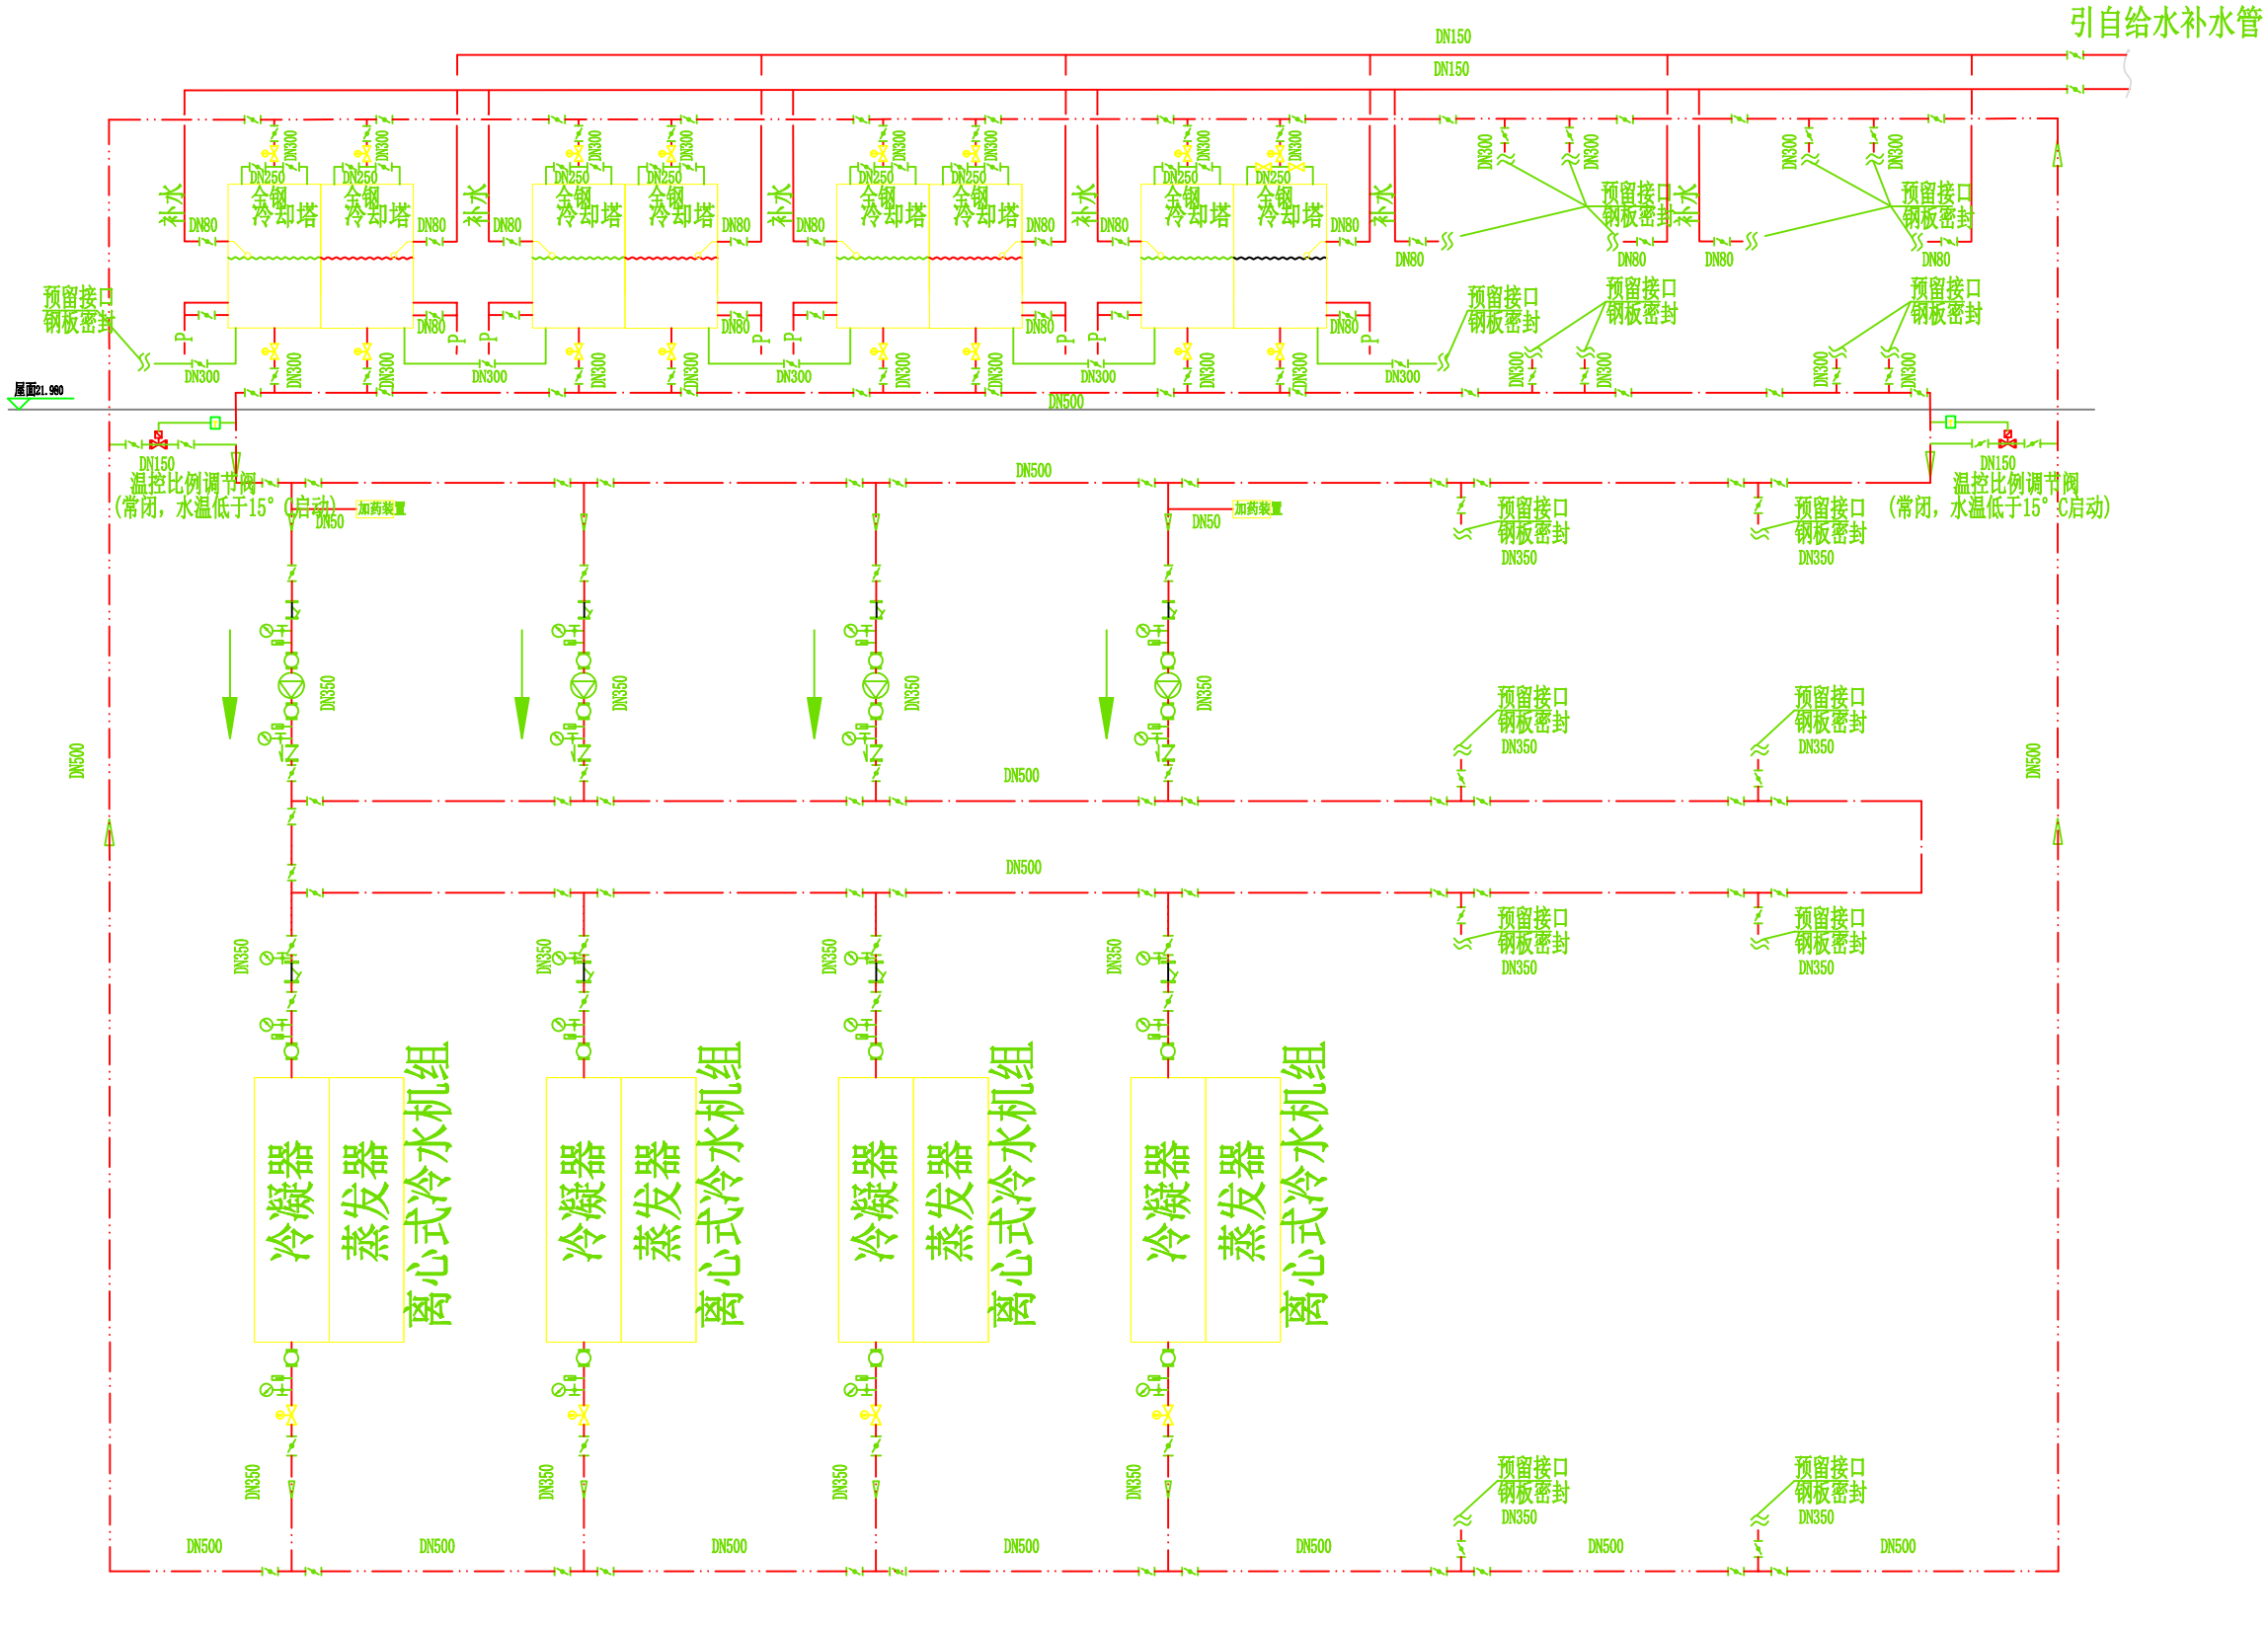

广东省电信规划设计院有限公司 工程设计证书编号：（甲级）A144011751						工程名称	华润集团新一代数据中心建设工程（一期） 1#数据中心楼
						建设单位	润联软件系统（深圳）有限公司
审 定	邓重秋		项目负责人	李卡卡		内 容	冷却水系统流程图
审 核	许新毅		专业负责人	许新毅			设计编号 130738-01-0006
校 对	李双磊		设 计	熊玮恺			设计阶段 空 施
							图 号 FK-07
							日 期 2014.06.13

建筑	结构	给排水	电气	采暖通风